



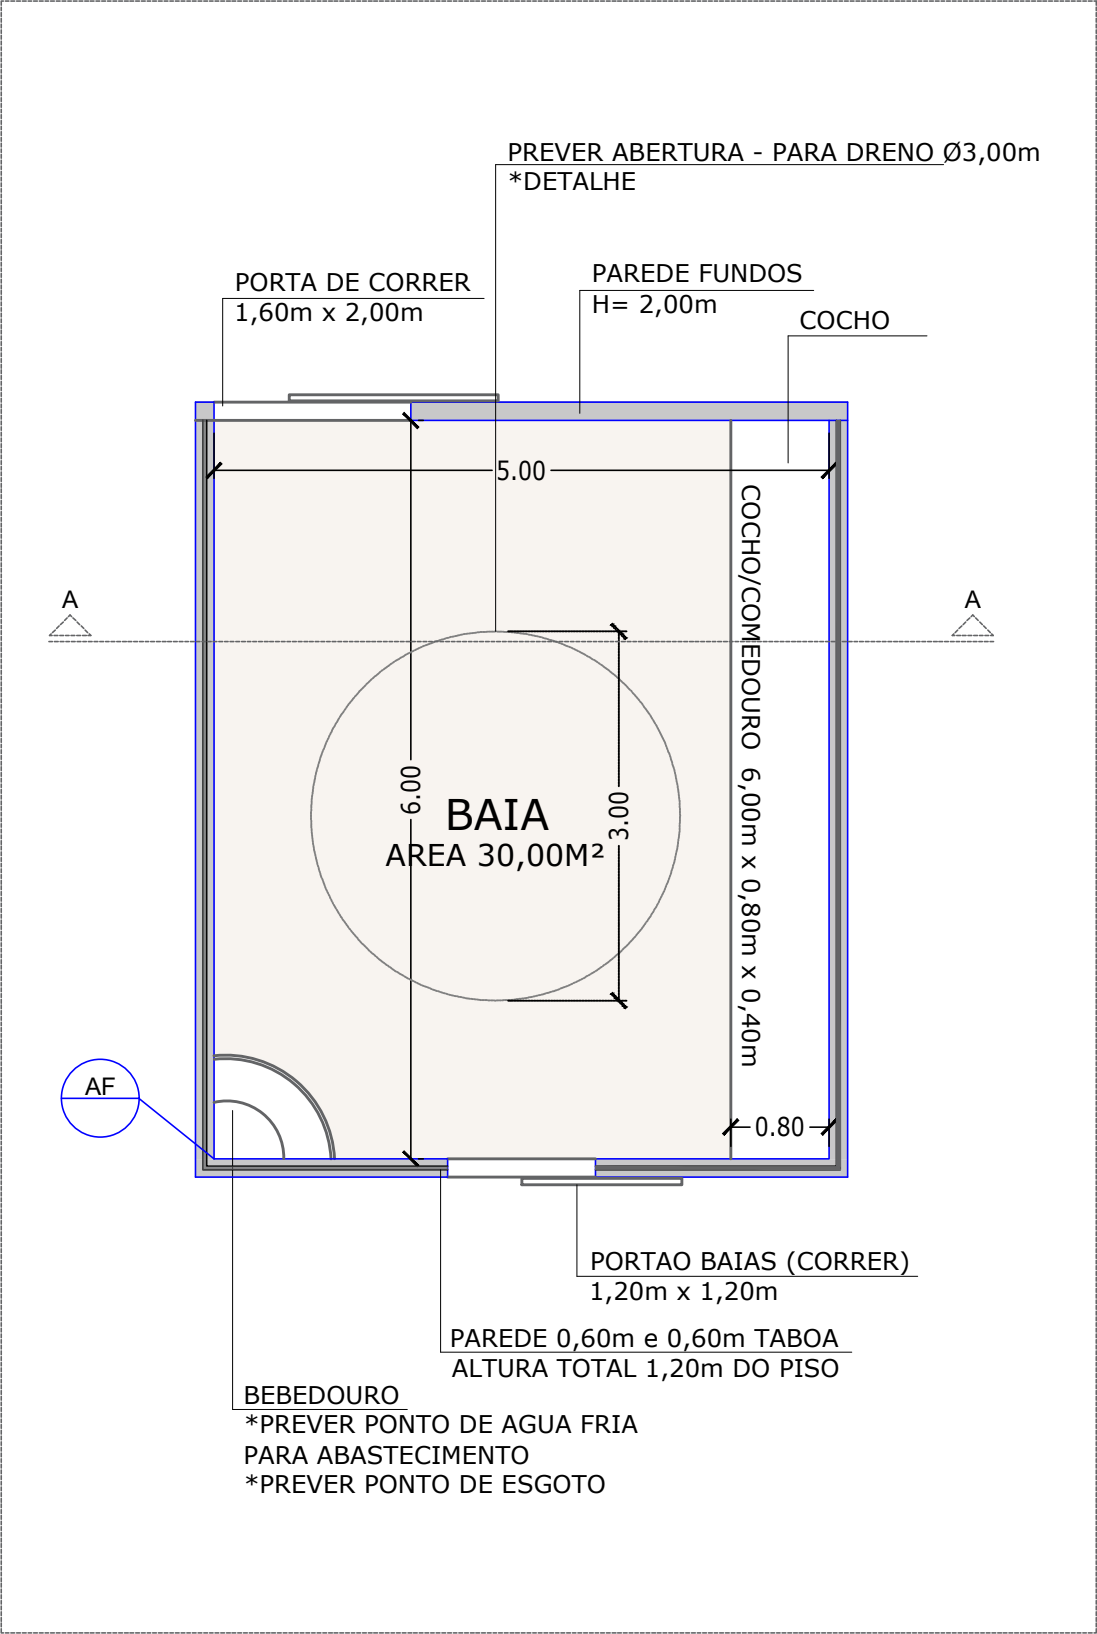

DETALHE BAIA

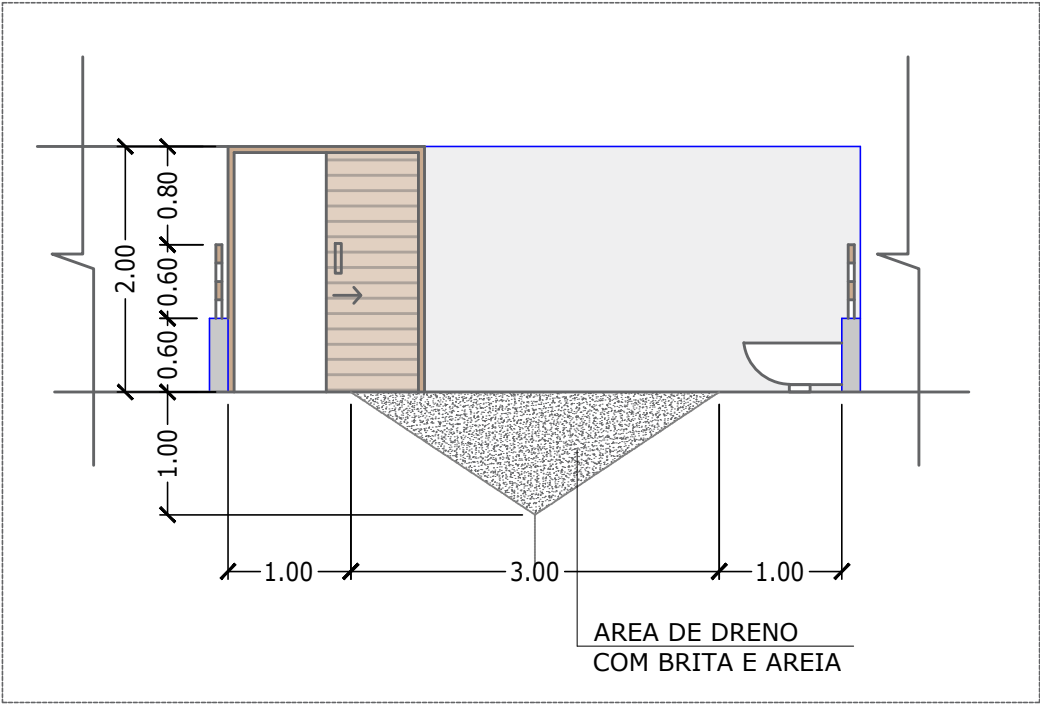

CORTE AA
DETALHE PARA DRENO

LEGENDA	
SÍMBOLO	ITEM
	PONTO DE LUZ NO TETO
	PONTO PARA ARANDELA ALTURA DO PISO ACABADO: 1,80m
	REFLETOR DE LED PARA ÁREA EXTERNA
	INTERRUPTOR PARALELO - CAIXA 4x2 ALTURA DO PISO ACABADO: 1,20m
	TOMADA BAIXA - CAIXA 4x2 ALTURA DO PISO ACABADO: 0,50m
	TOMADA MÉDIA - CAIXA 4x2 ALTURA DO PISO ACABADO: 1,10m

OBSERVAÇÕES:
1. CONSIDERAR TEMPERATURA DE COR 3000K PARA TODOS AMBIENTES.

BAIAS GRUPO MONICA

FAZENDA SANTA MONICA - ITU/SP

ESC. INDICADAS

DATA MAIO/2026

PROPRIETARIO: GRUPO MONICA

DETALHES BAIAS

REV. 00

NOTAS DE OBSERVAÇÃO:

