



PLANTA DA COBERTURA

1:75

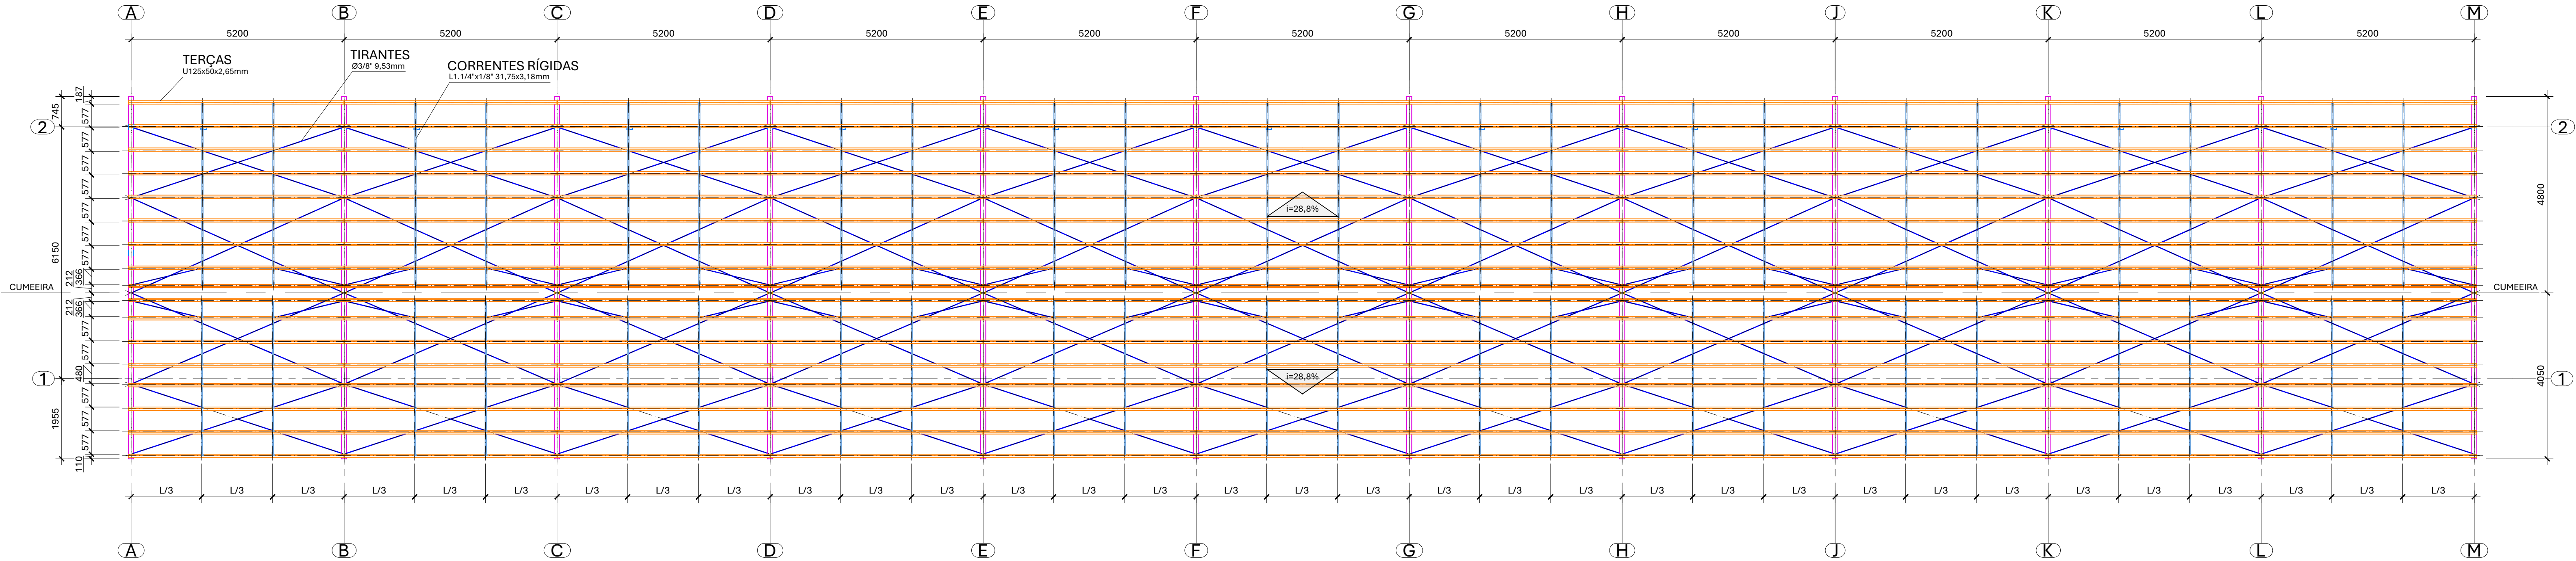


PLANTA DE TRAVAMENTO DO BANZO INFERIOR




1:75

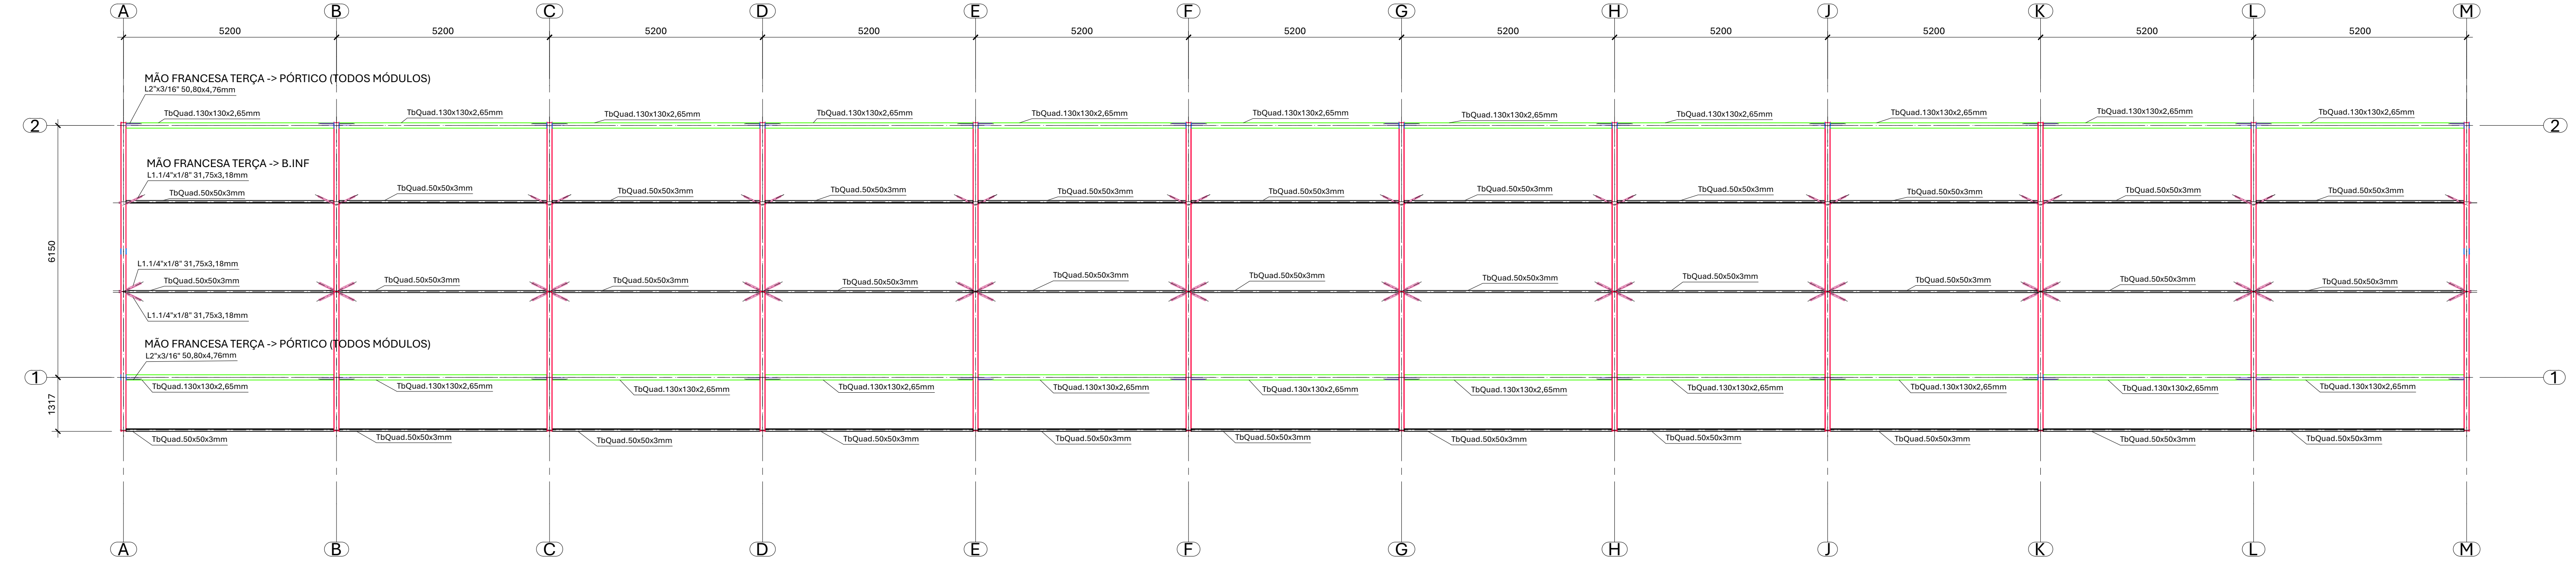

MÃO FRANCESA TERÇA -> PÓRTICO

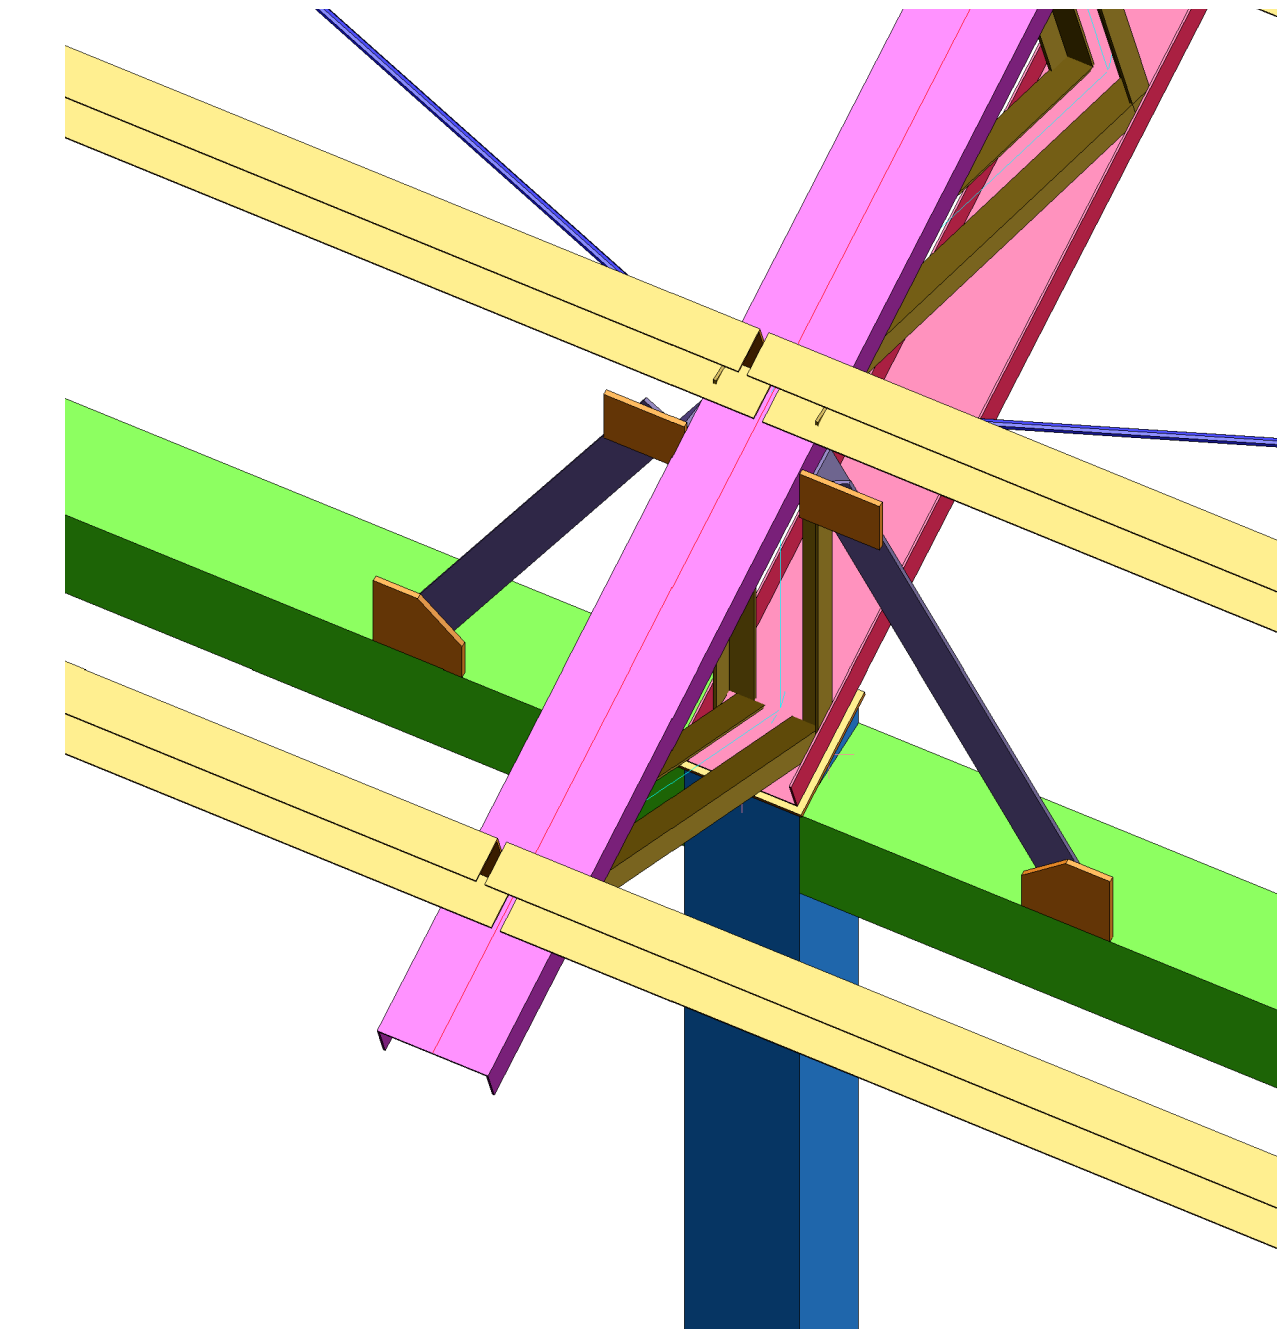

MÃO FRANCESA TERÇA -> B.INF

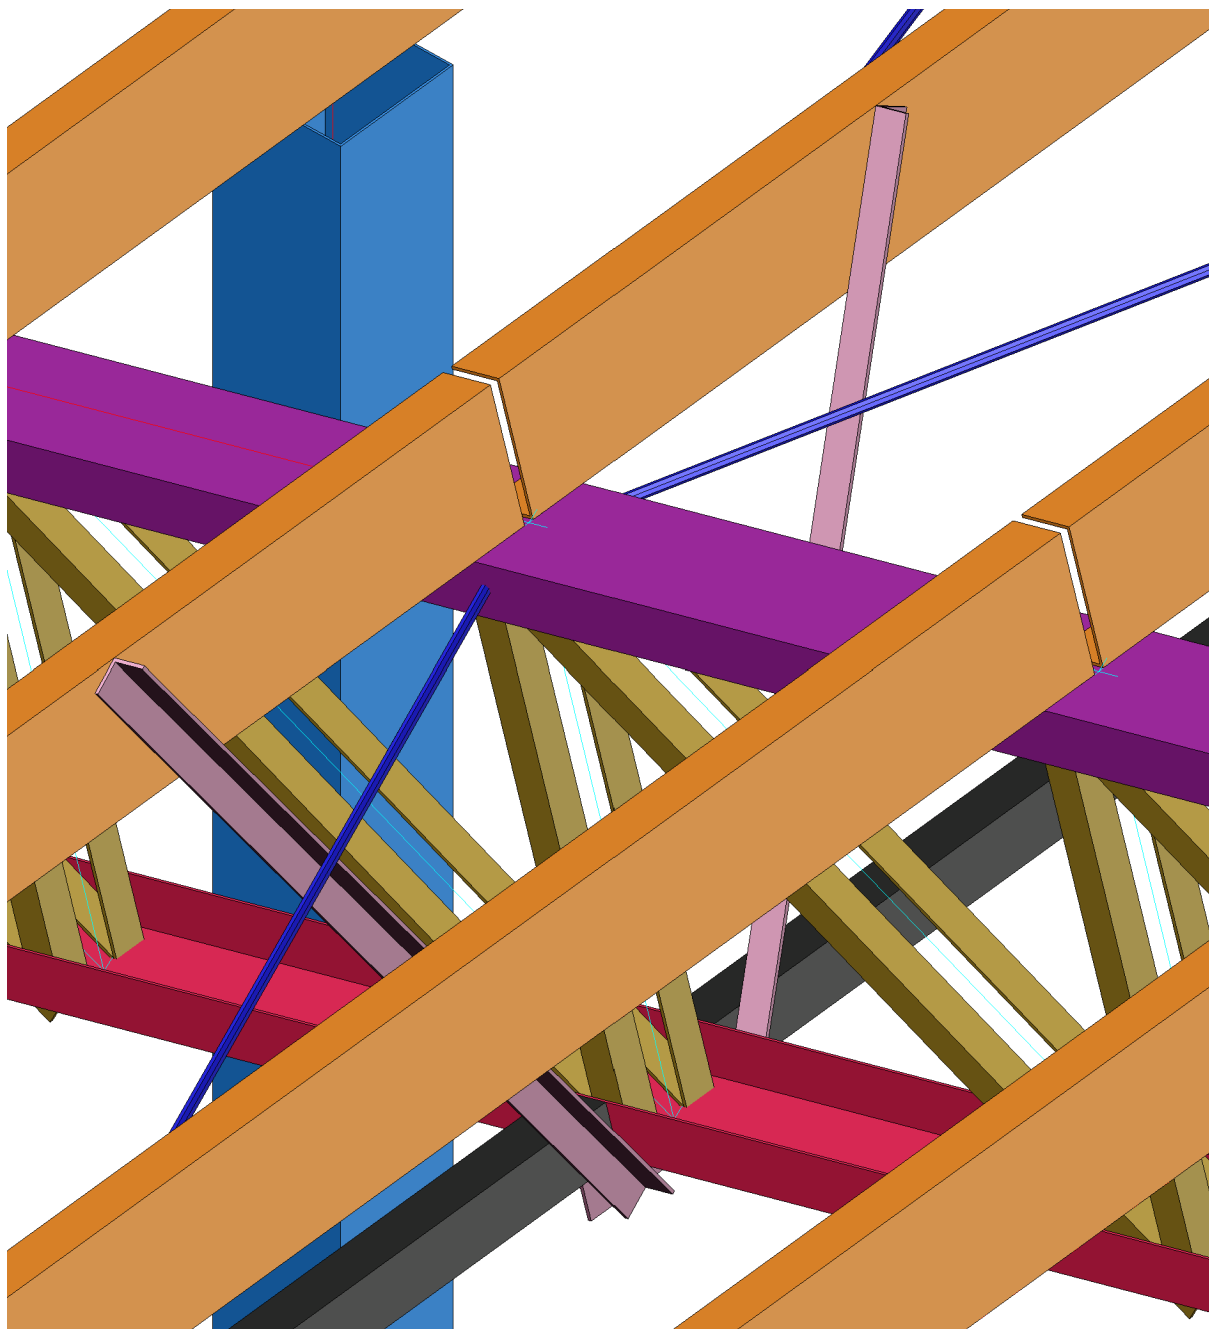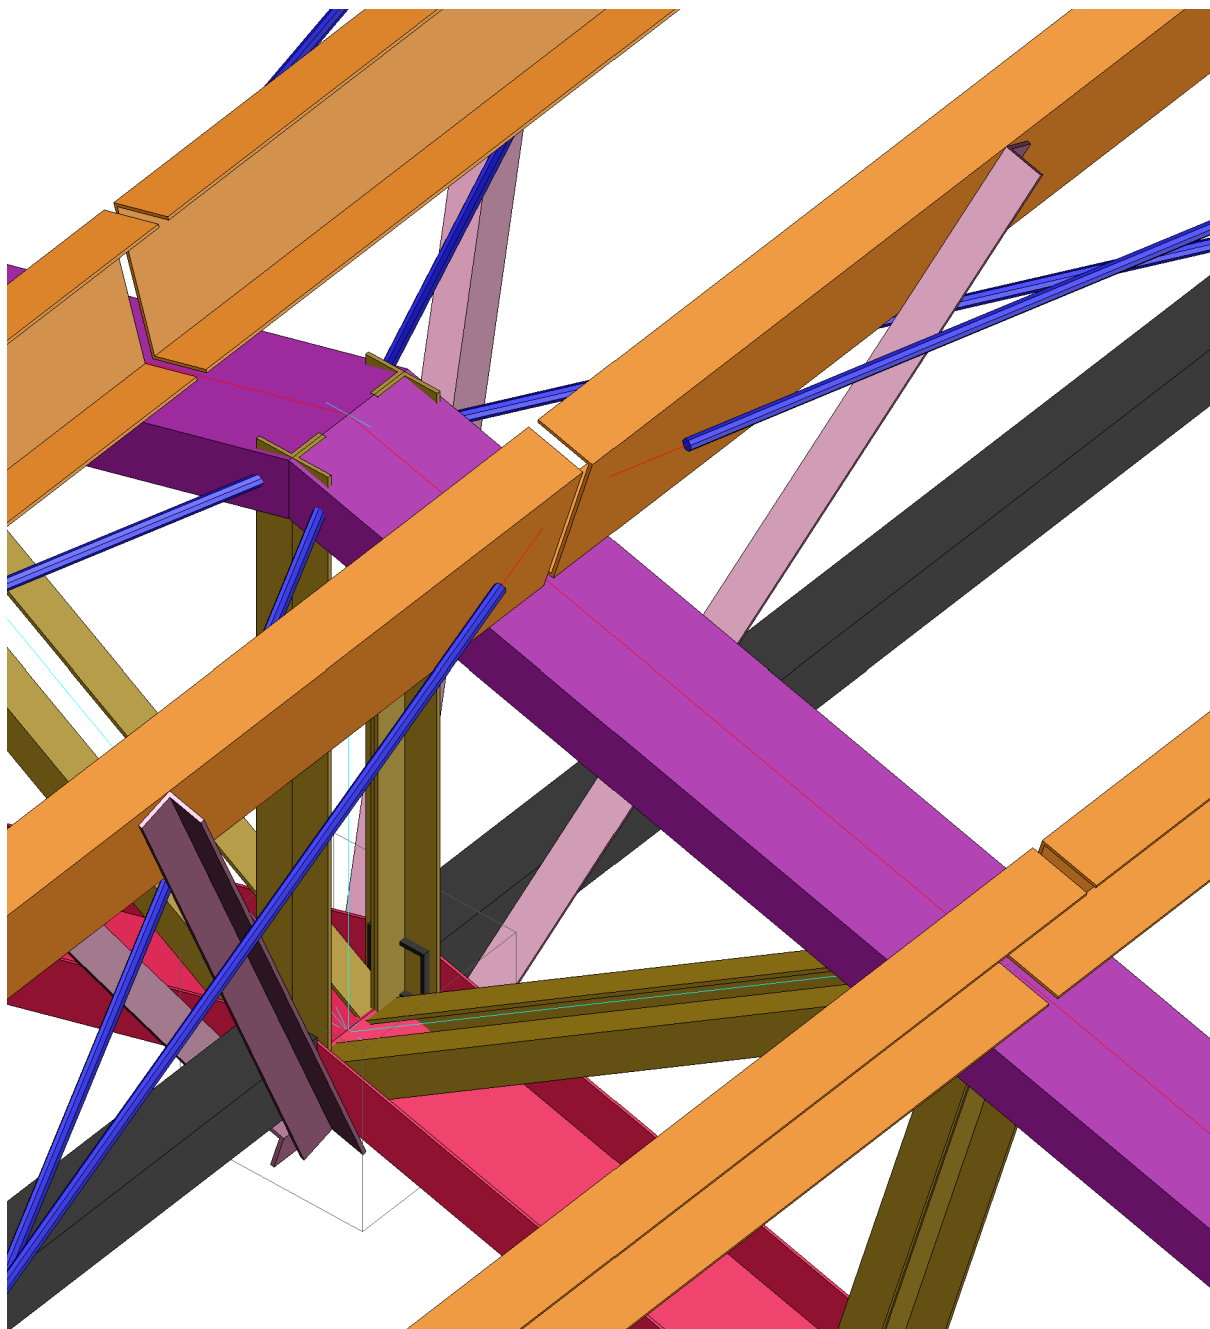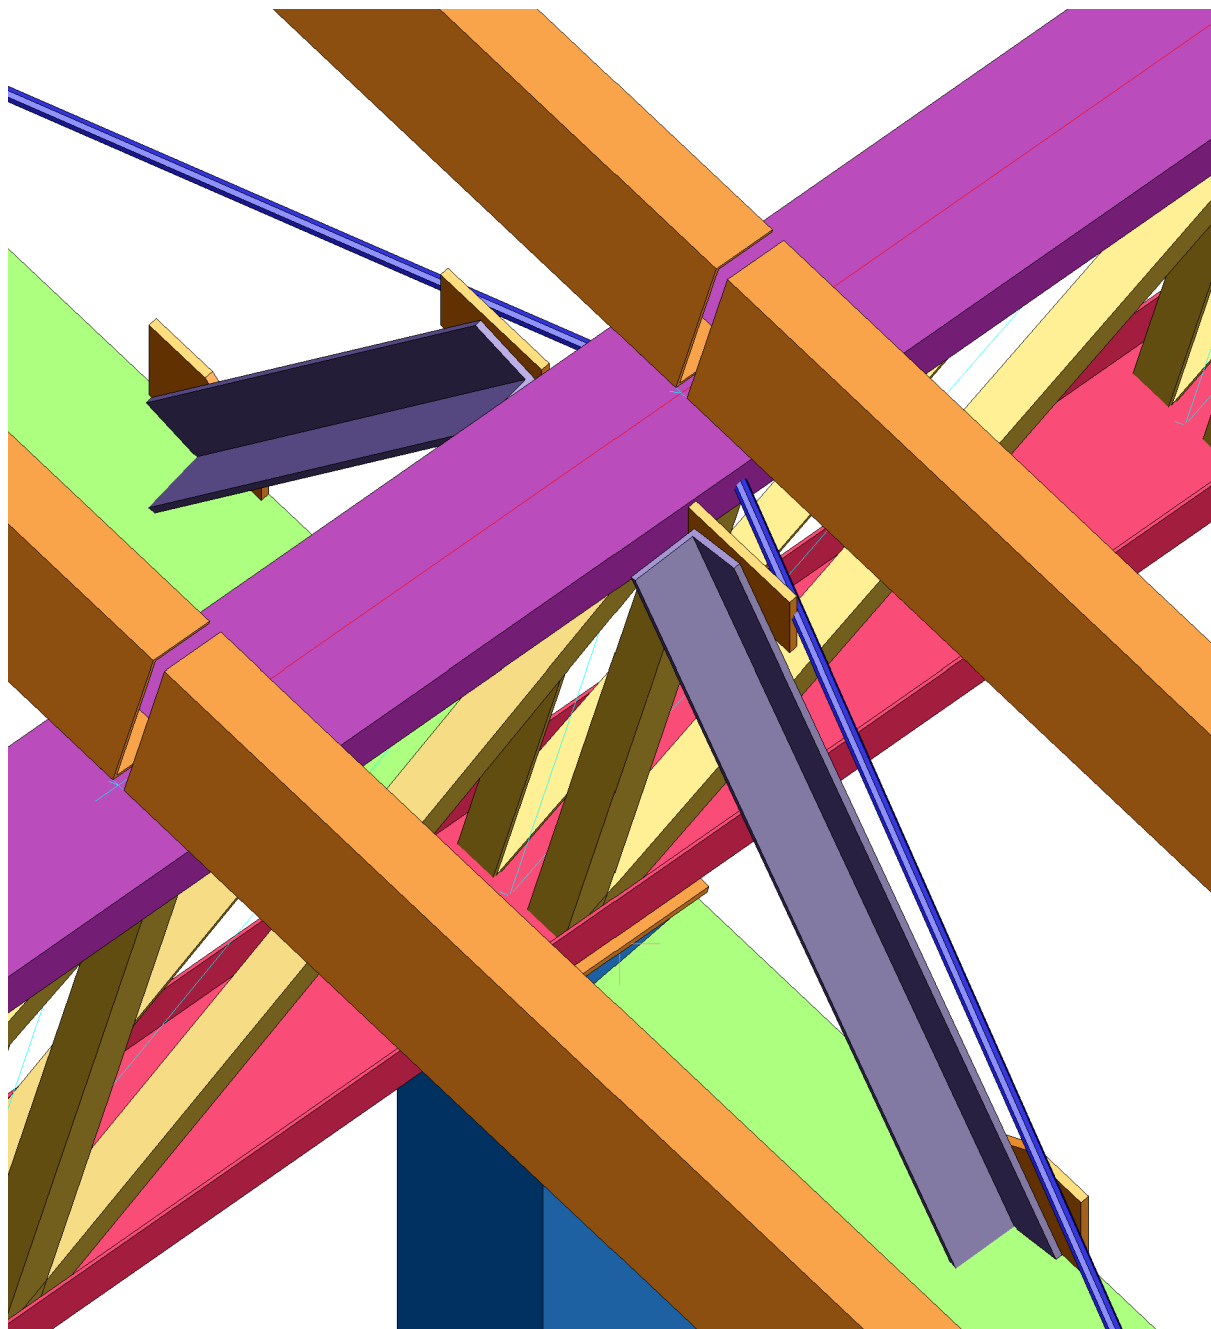

- NOTAS METÁLICAS:
- LAMINADOS: ASTM A572 - GRAU 50 ($f_y \geq 34,5 \text{ kN/cm}^2$; $f_u \geq 45 \text{ kN/cm}^2$);
 - PERFIS DOBRADOS E CHAPAS: ASTM A36 ($f_y \geq 25 \text{ kN/cm}^2$; $f_u \geq 40 \text{ kN/cm}^2$);
 - FIXAÇÃO DAS CHAPAS BASE ATRAVÉS DE GRAPAS (A36) e/ou BARRAS ROSCADAS SAE1045 ($f_y \geq 31 \text{ kN/cm}^2$; $f_u \geq 56 \text{ kN/cm}^2$);
 - LIGAÇÕES PARAFUSADAS: ASTM A325 ($f_y \geq 63,5 \text{ kN/cm}^2$; $f_u \geq 83,5 \text{ kN/cm}^2$);
 - SOLDAS:
 - CONFORME NORMA AWS: E-70XY ($f_u \geq 48,5 \text{ kN/cm}^2$);
 - FILETES NO PERÍMETRO TOTAL - $\geq$ MAIOR ENTRE 5mm e 1" mm (SEDO τ A MENOR ESPESSURA DAS CHAPAS A SEREM CONECTADAS);
 - PINTURA:
 - PREPARO DA SUPERFÍCIE COM LIMPEZA MANUAL DESGROSSADORA, DECAPANTE E DESENGORDURANTE, SEGUIDA DE APLICAÇÃO DE FUNDO PREPARADOR COM 80 MICRONS EM BASE EPÓXI E POSTERIORMENTE APLICAÇÃO DE ACABAMENTO COM 40 MICRONS DE PINTURA EM BASE POLIURETANO TOTALIZANDO 120 MICRONS DE ESPESSURA SECA;
 - RELAÇÃO DE NORMAS ADOTADAS NO PROJETO: NBR8800, NBR9971, NBR14762, NBR5884, ISO6982, NBR6118, NBR6120, NBR6122, NBR6123;
 - COTAS ALTIMÉTRICAS EM METROS;
 - COTAS PLANIMÉTRICAS EM MILÍMETROS, EXCETO ONDE INDICADO;
 - VER LISTA DE MATERIAIS EM ANEXO;
 - LISTA DE MATERIAIS E APENAS INDICATIVA, SENDO RESPONSABILIDADE DO FORNECEDOR A VERIFICAÇÃO DA MEDIDA PARA ELABORAR SUA PROPOSTA;
 - TODOS OS CORTES DE MATERIAL DEVERÃO SER CONFIRMADOS APÓS A FIXAÇÃO DAS CHAPAS E PÉ DIREITOS;
 - CONFIRMAR E VALIDAR MEDIDAS IN LOCO.

00	JUN/2026	EMISSÃO INICIAL	
REVISÃO	DATA	DESCRIÇÃO	
PROJETO ESTRUTURAL - CONSTRUÇÃO DE BAIS			
ASSUNTO:	PLANTA DA COBERTURA E TRAVAMENTOS DO BANZO INFERIOR		
LOCAL:	FAZENDA SANTA MONICA - ITU - S.P.		
CLIENTE:	GRUPO MONICA		
PROJ. N.º	1092/26	ESCALA:	IND.
DES. N.º	1092-26-005	DATA:	JUN/2026
PROJETO:	ENG.º PAULO ROBERTO LEONELLO	CREA:	57577-1
DESENHO:	ENG.º LUCAS LEONELLO	CREA:	5089791299

LEONELLO
PROJETOS E CONSULTORIA TÉCNICA LTDA
e-mail: contato@leonelloprojetos.eng.br

FOLHA:
005