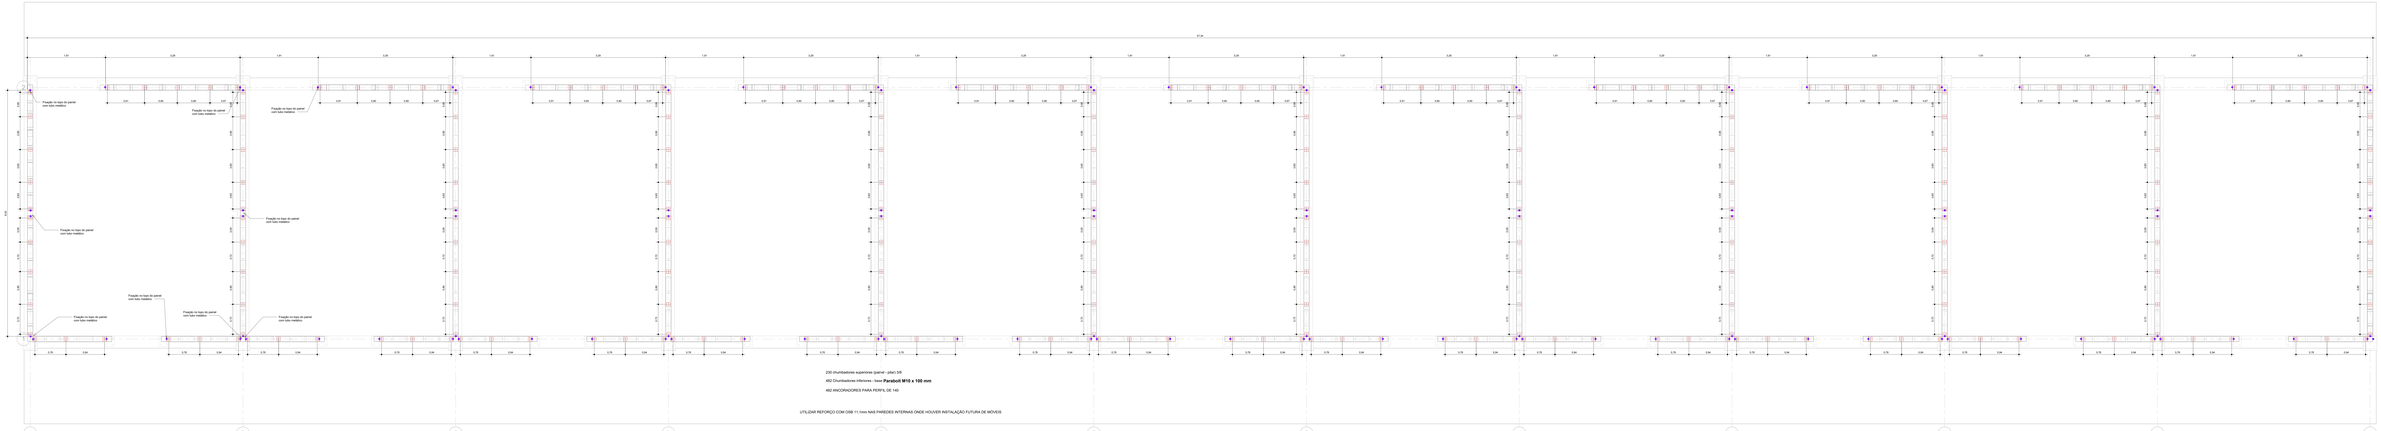

230 chumbadores superiores (painel - piso) 3/8

462 Chumbadores inferiores - base **Parabolt M10 x 100 mm**

462 ANCORAGHOORES PARA PERFIL DE 140

UTILIZAR REFORÇO COM OSB 11.1mm NAS PAREDES INTERNAS ONDE HOUVER INSTALAÇÃO FUTURA DE MOVEIS